

अर्जदार श्री विपीन नारायण सागर. योनी मोजे - वारदोली, तालुका - पनवेल. पेथील. ग. नं. ९१/१ ची पोट. हिस्सा भोजणसिटी दिनांक ६/१२ २०१० रोजी कोलोल्या मोजणी अर्जान्वये मोजणी करून तयार केकेला मोजणी नकाशा.

मोजणीचे कारण :- अ. ता. पोट हिस्सा :- अर्जदार श्री विपीन नारायण सागर. योनी मोजे - वारदोली, तालुका - पनवेल. पेथील. ग. नं. ९१/१ ची पोट. हिस्सा भोजणसिटी दिनांक ६/१२ २०१० रोजी कोलोल्या मोजणी अर्जान्वये मोजणी करून तयार केकेला मोजणी नकाशा.

अ. ता. पो. हि. मो. र. नं. ३८२/०११



गाव - वारदोली
तालुका - पनवेल
जिल्हा - रायगड

अभिलेखाचा प्रकार
फाळणी

सर्व्हे नंबर
९१/१


मो. र. नं. - 382/011

मोजणीचे कारण -

अर्जदार श्री विपीन नारायण सागर. योनी मोजे - वारदोली, तालुका - पनवेल. पेथील. ग. नं. ९१/१ ची पोट. हिस्सा भोजणसिटी दिनांक ६/१२ २०१० रोजी कोलोल्या मोजणी अर्जान्वये मोजणी करून तयार केकेला मोजणी नकाशा.

समजुतीच्या टिपा

- N नवीन खुणा
- F कायम दगड
- झाड
- एक मोटेची विहीर
- दोन मोटेची विहीर
- विहिर
- पायऱ्यांची विहीर
- कोरडी विहीर परंतु दुरुस्त
- जुनी कोरडी विहीर नोंदुरुस्त
- E इलेक्ट्रिक इंजिन असलेली विहीर
- D डीझेल इंजिन असलेली विहीर
- T टेलीफोन खांब
- V विजेचा खांब
- V विजेचा दिवा
- सर्व्हे/गट नं ची हद
- हिस्स्याची हद
- याप्रमाणे वहिवाट
- * / * तारेचे कुंपण
- पायवाट
- = गाडी रस्ता
- बांधकाम
- प्लॉटची हद
- भितीचे कुंपण
- संपादित क्षेत्र

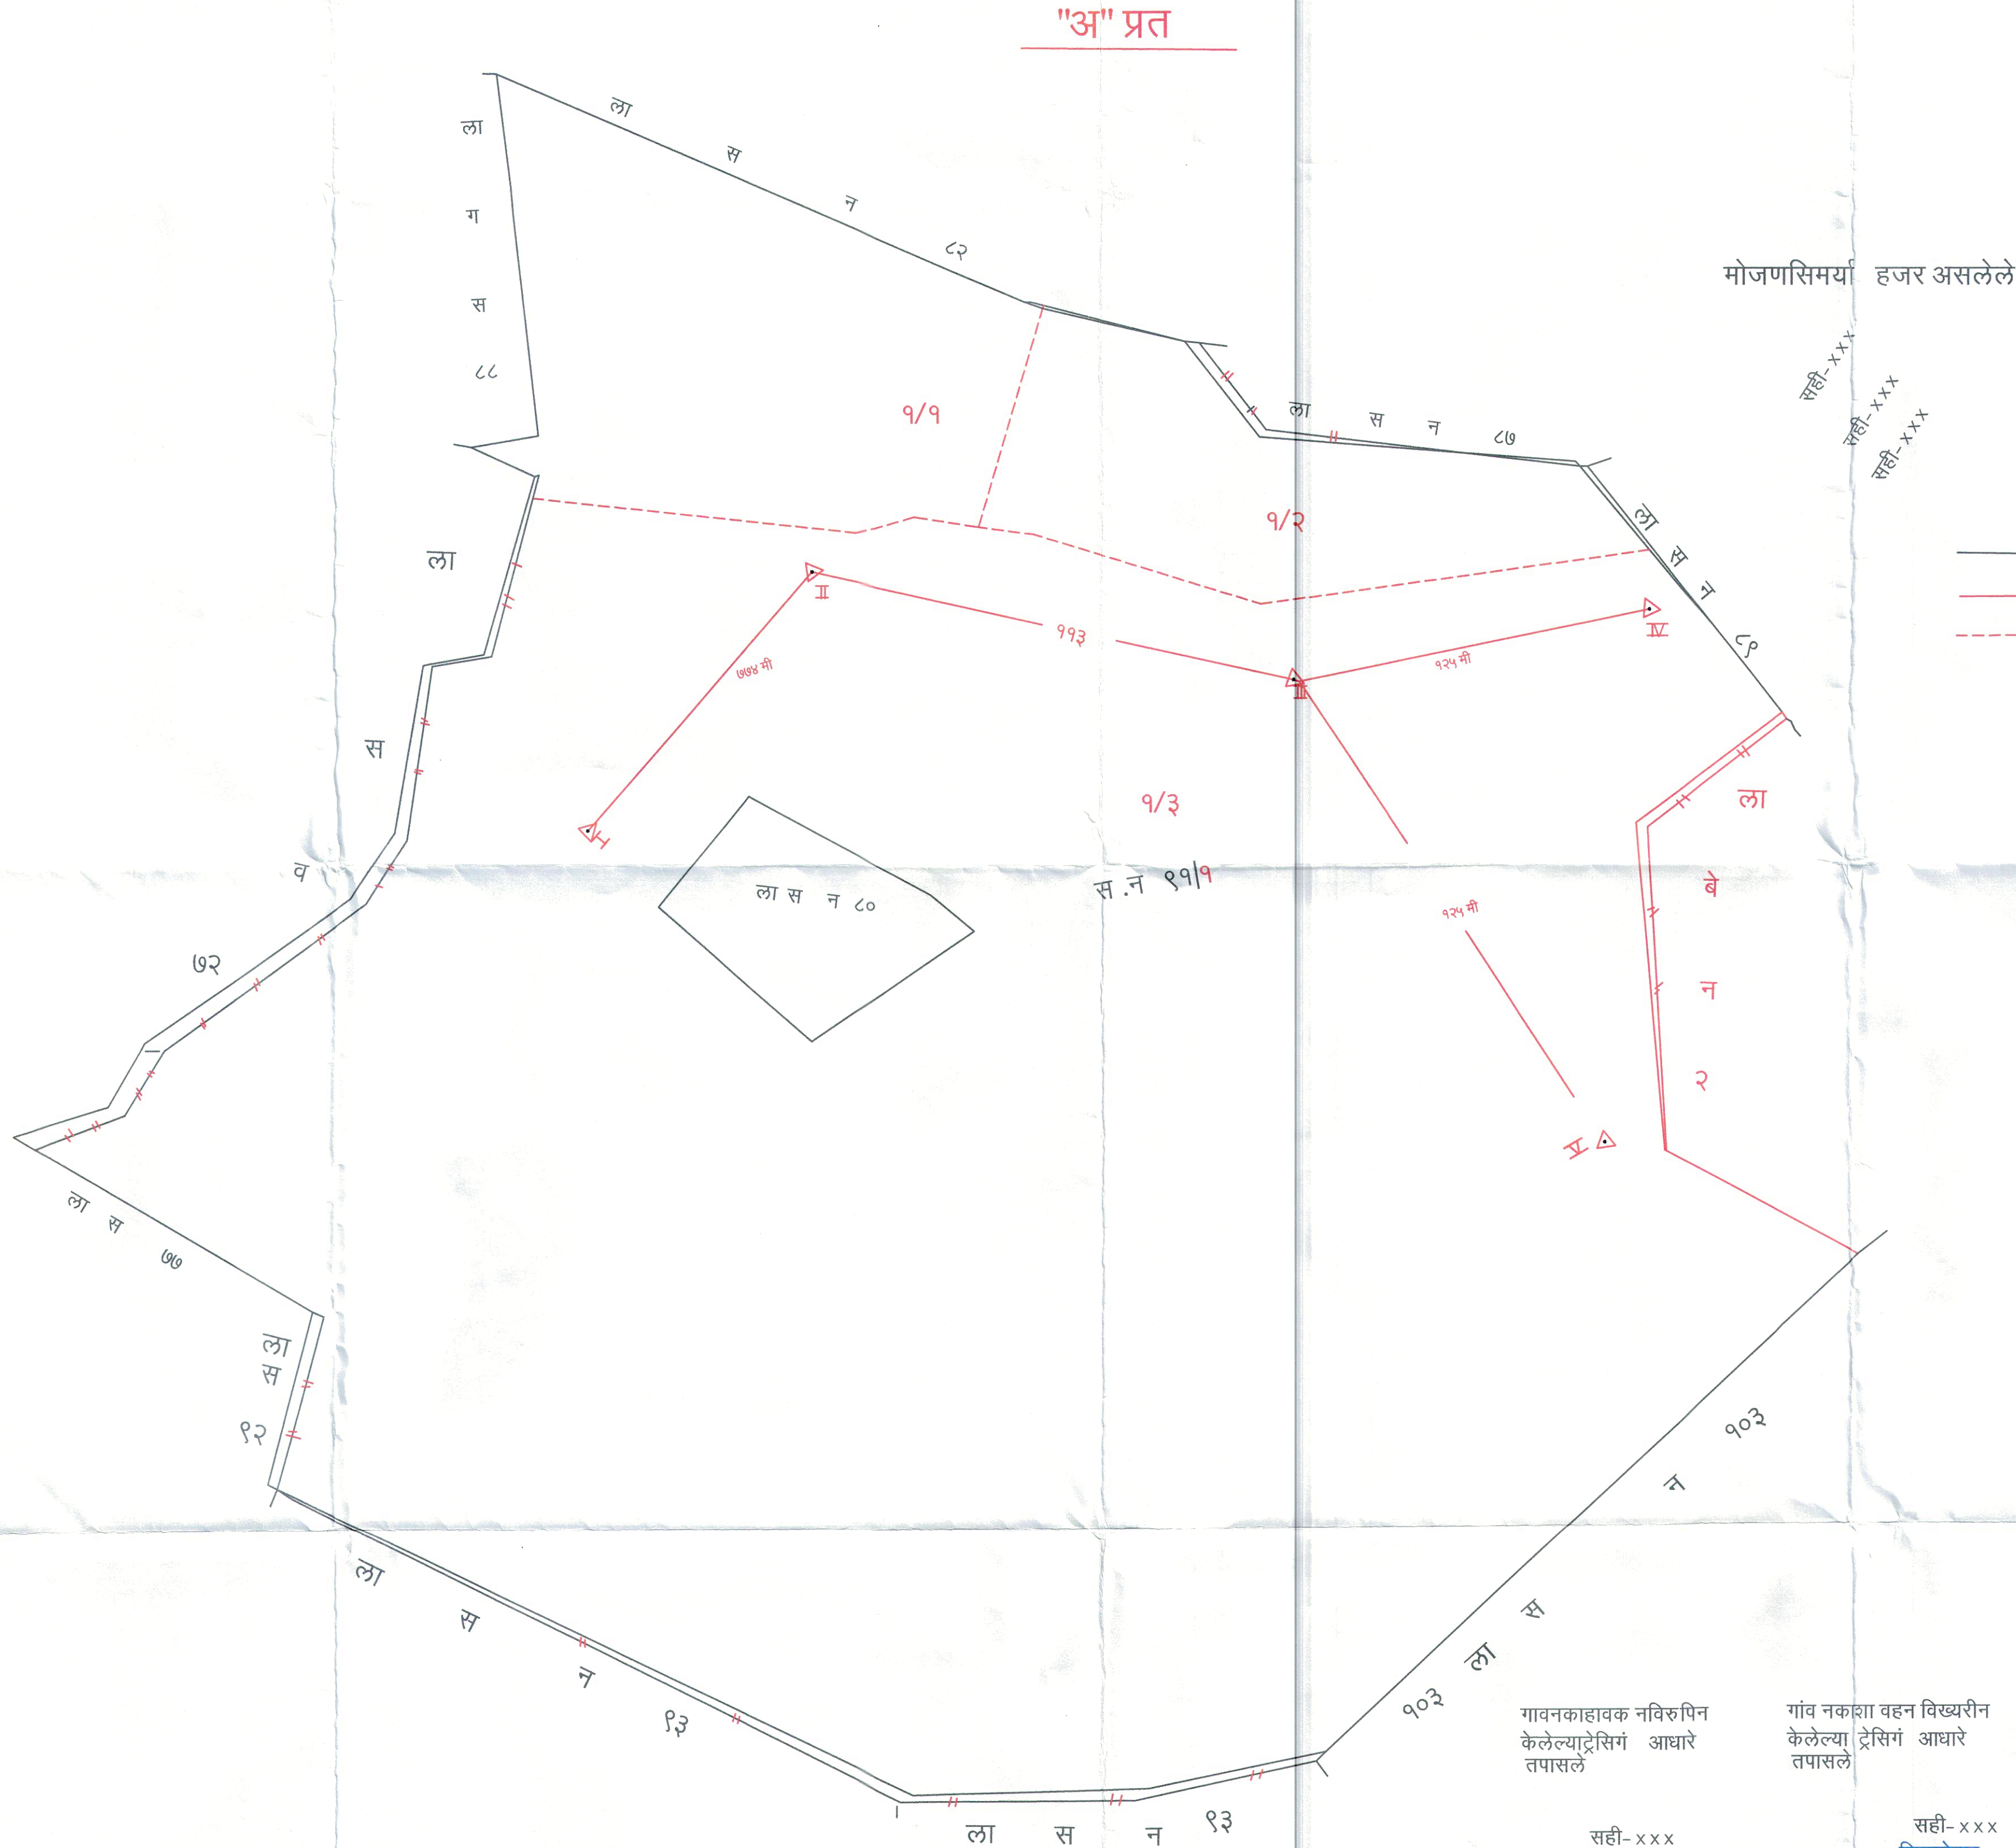

समजुताच्या टिपा
— याप्रमाणे अभिलेखानुसार स. न. ची हदद असे
— याप्रमाणे अभिलेखानुसार हि. न. ची हदद असे
--- याप्रमाणे अर्जदार व सहहिस्सेदार मोजणीवोकी आपली वहिवाट दाखवित असे.


प्रमाण :- १ : १ ०० ०

मोजणी करणार :- सही- x x x

श्री . स.र.पाटारा.(प-भू.)

मोजणी दिनांक :- ३१/१२/२०११

Satish Madhav Sangle
Digitally signed by Satish Madhav Sangle
Date: 2021.10.20 16:38:52 +05'30'

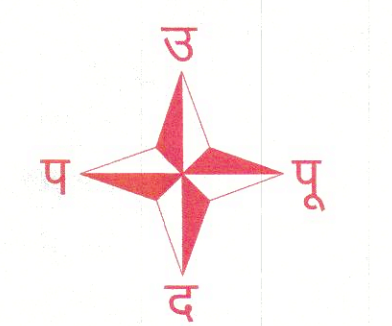

प्रमाण :- 1:1000

मोजणीचा दिनांक - 3/2/2011
हद दाखविल्या दिनांक -
मोजणी करणार - श्री . स.र.पाटारा.(प-भू.)

महाराष्ट्र शासन
भूमि अभिलेख विभाग

अर्जदारचे नाव	पार्ष्व	अर्ज क्र.	
खरी नक्कल	१२०	नक्कल अर्ज प्राप्त दि.	१२/१२/२०११
कामद फी	३०	नक्कल तयार करणार	१२/१२/२०११
शोध फी	३०	नक्कल तयार करणार	१२/१२/२०११
एकूण फी	९३०	नक्कल तयार करणार	१२/१२/२०११