



PHYSICAL / ACTUAL SURVEY

VILLAGE:- ADIVALI & DHANSAR
TAL:- PANVEL
DIST:- RAIGAD.

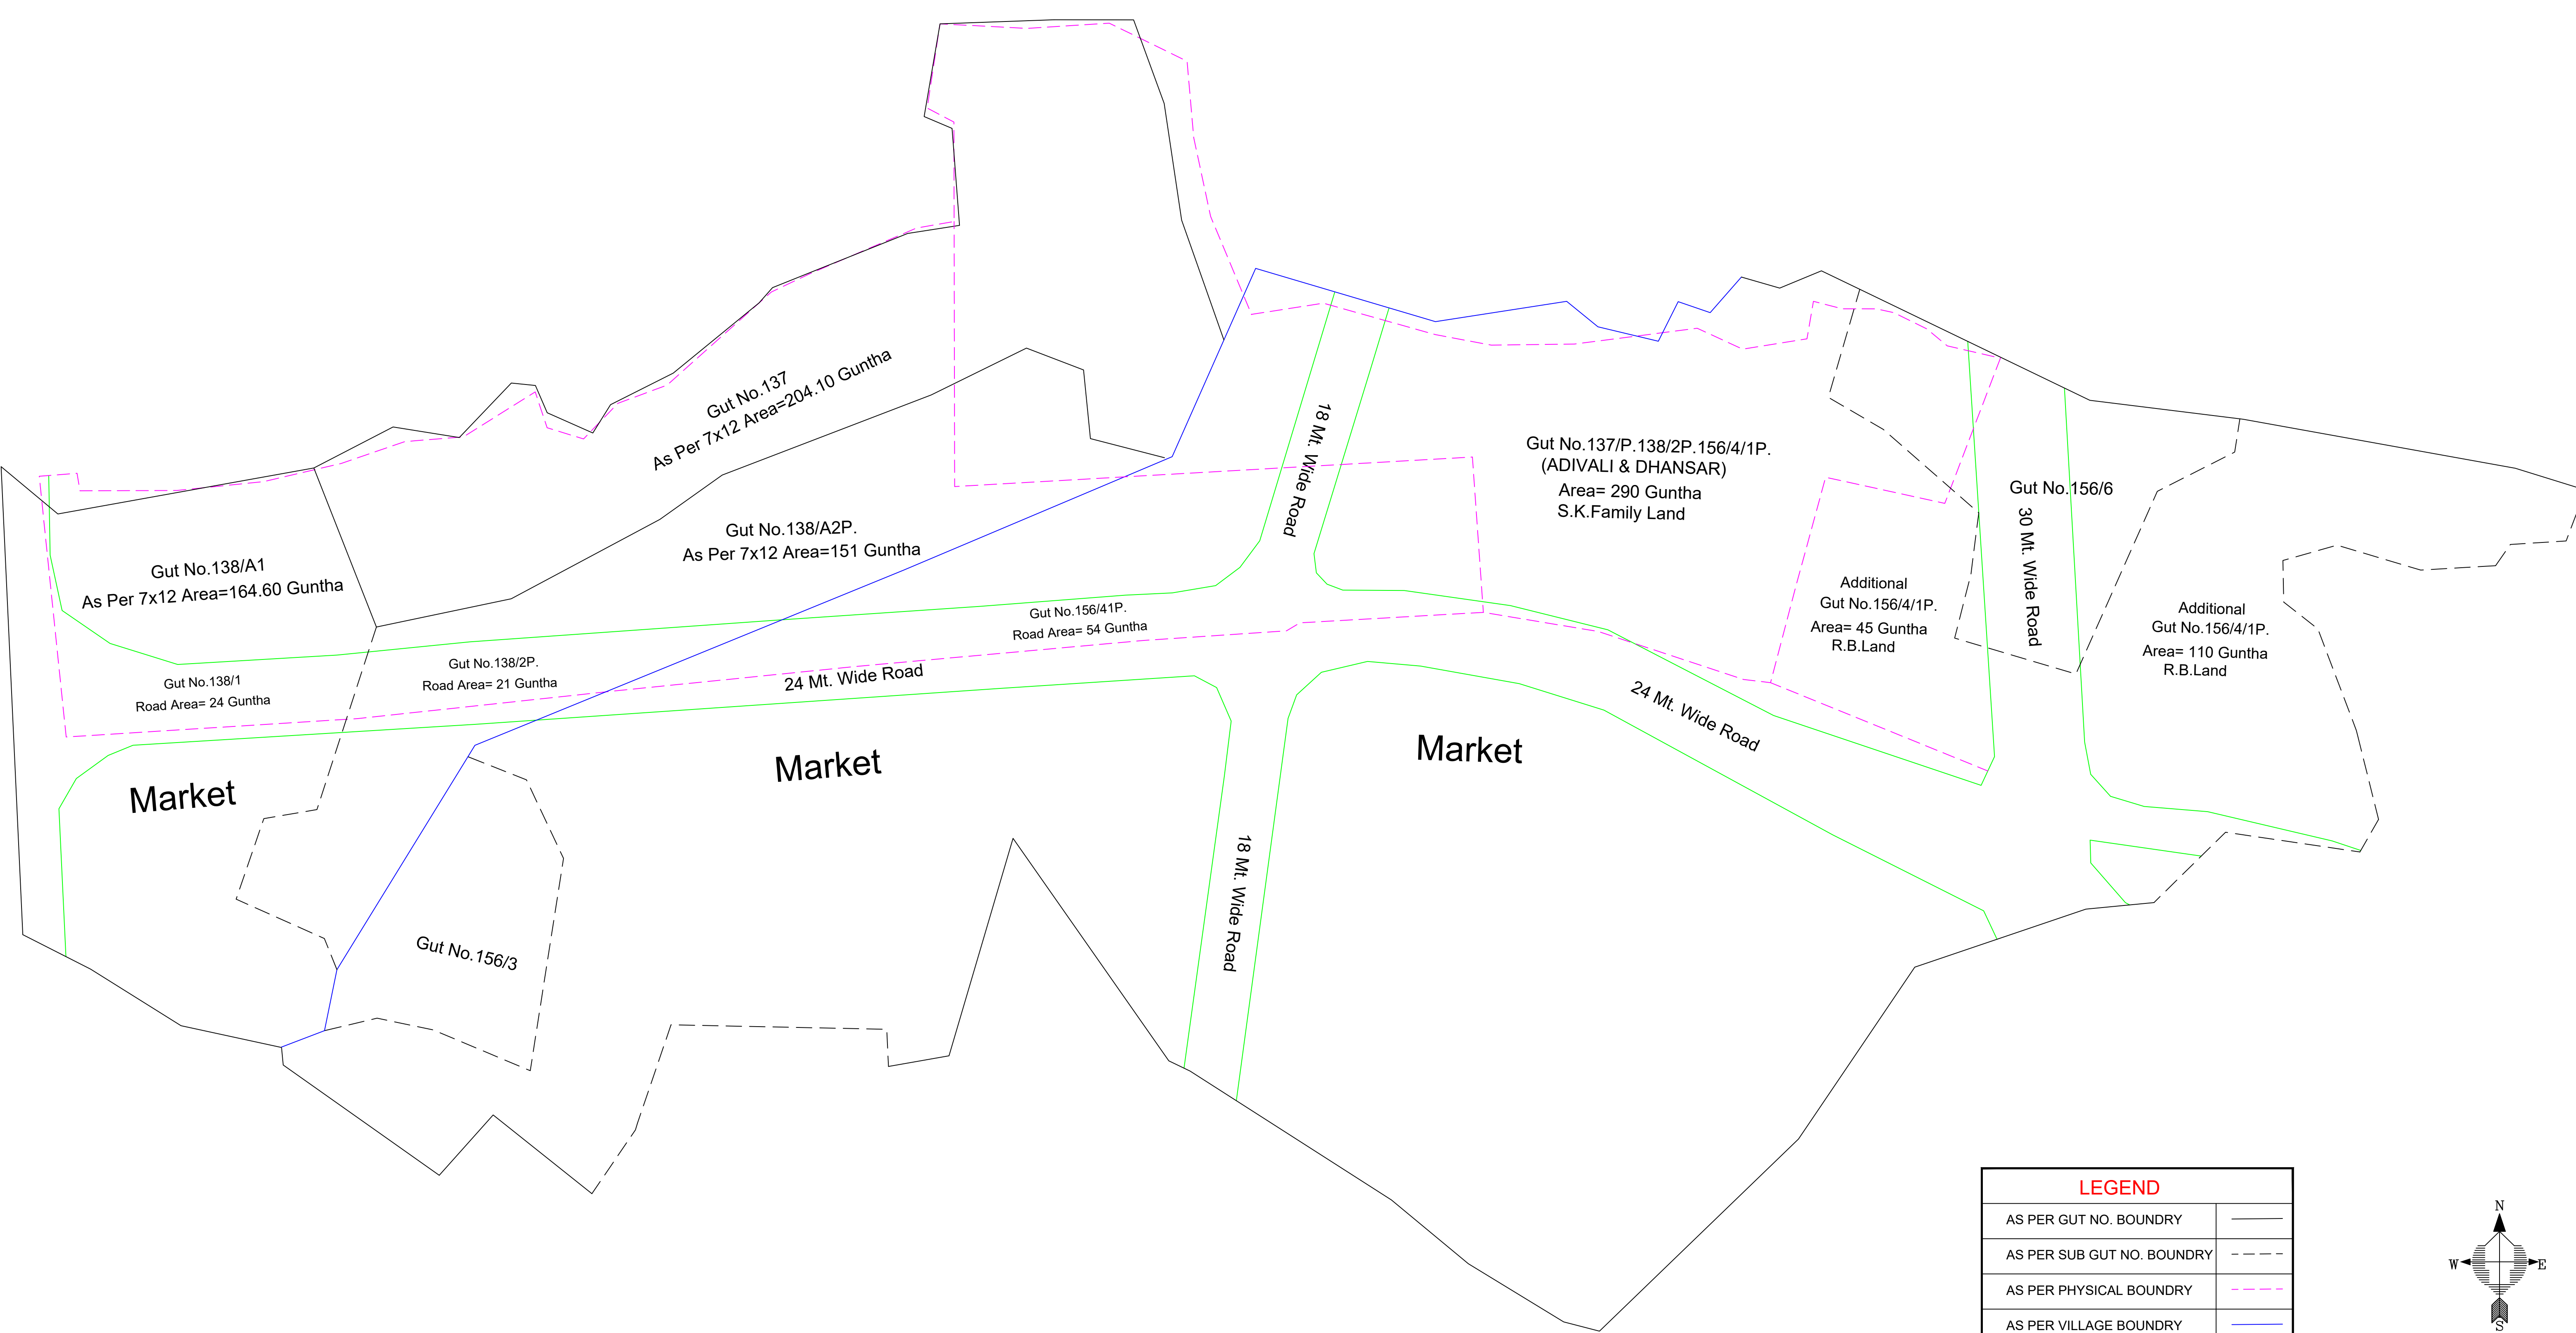

LEGEND	
AS PER GUT NO. BOUNDRY	
AS PER SUB GUT NO. BOUNDRY	
AS PER PHYSICAL BOUNDRY	
AS PER VILLAGE BOUNDRY	
DP ROAD	

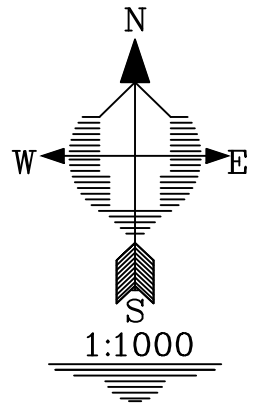

22-06-2025