



PHYSICAL / ACTUAL SURVEY

VILLAGE:- ADIVALI & DHANSAR
TAL:- PANVEL
DIST:- RAIGAD.

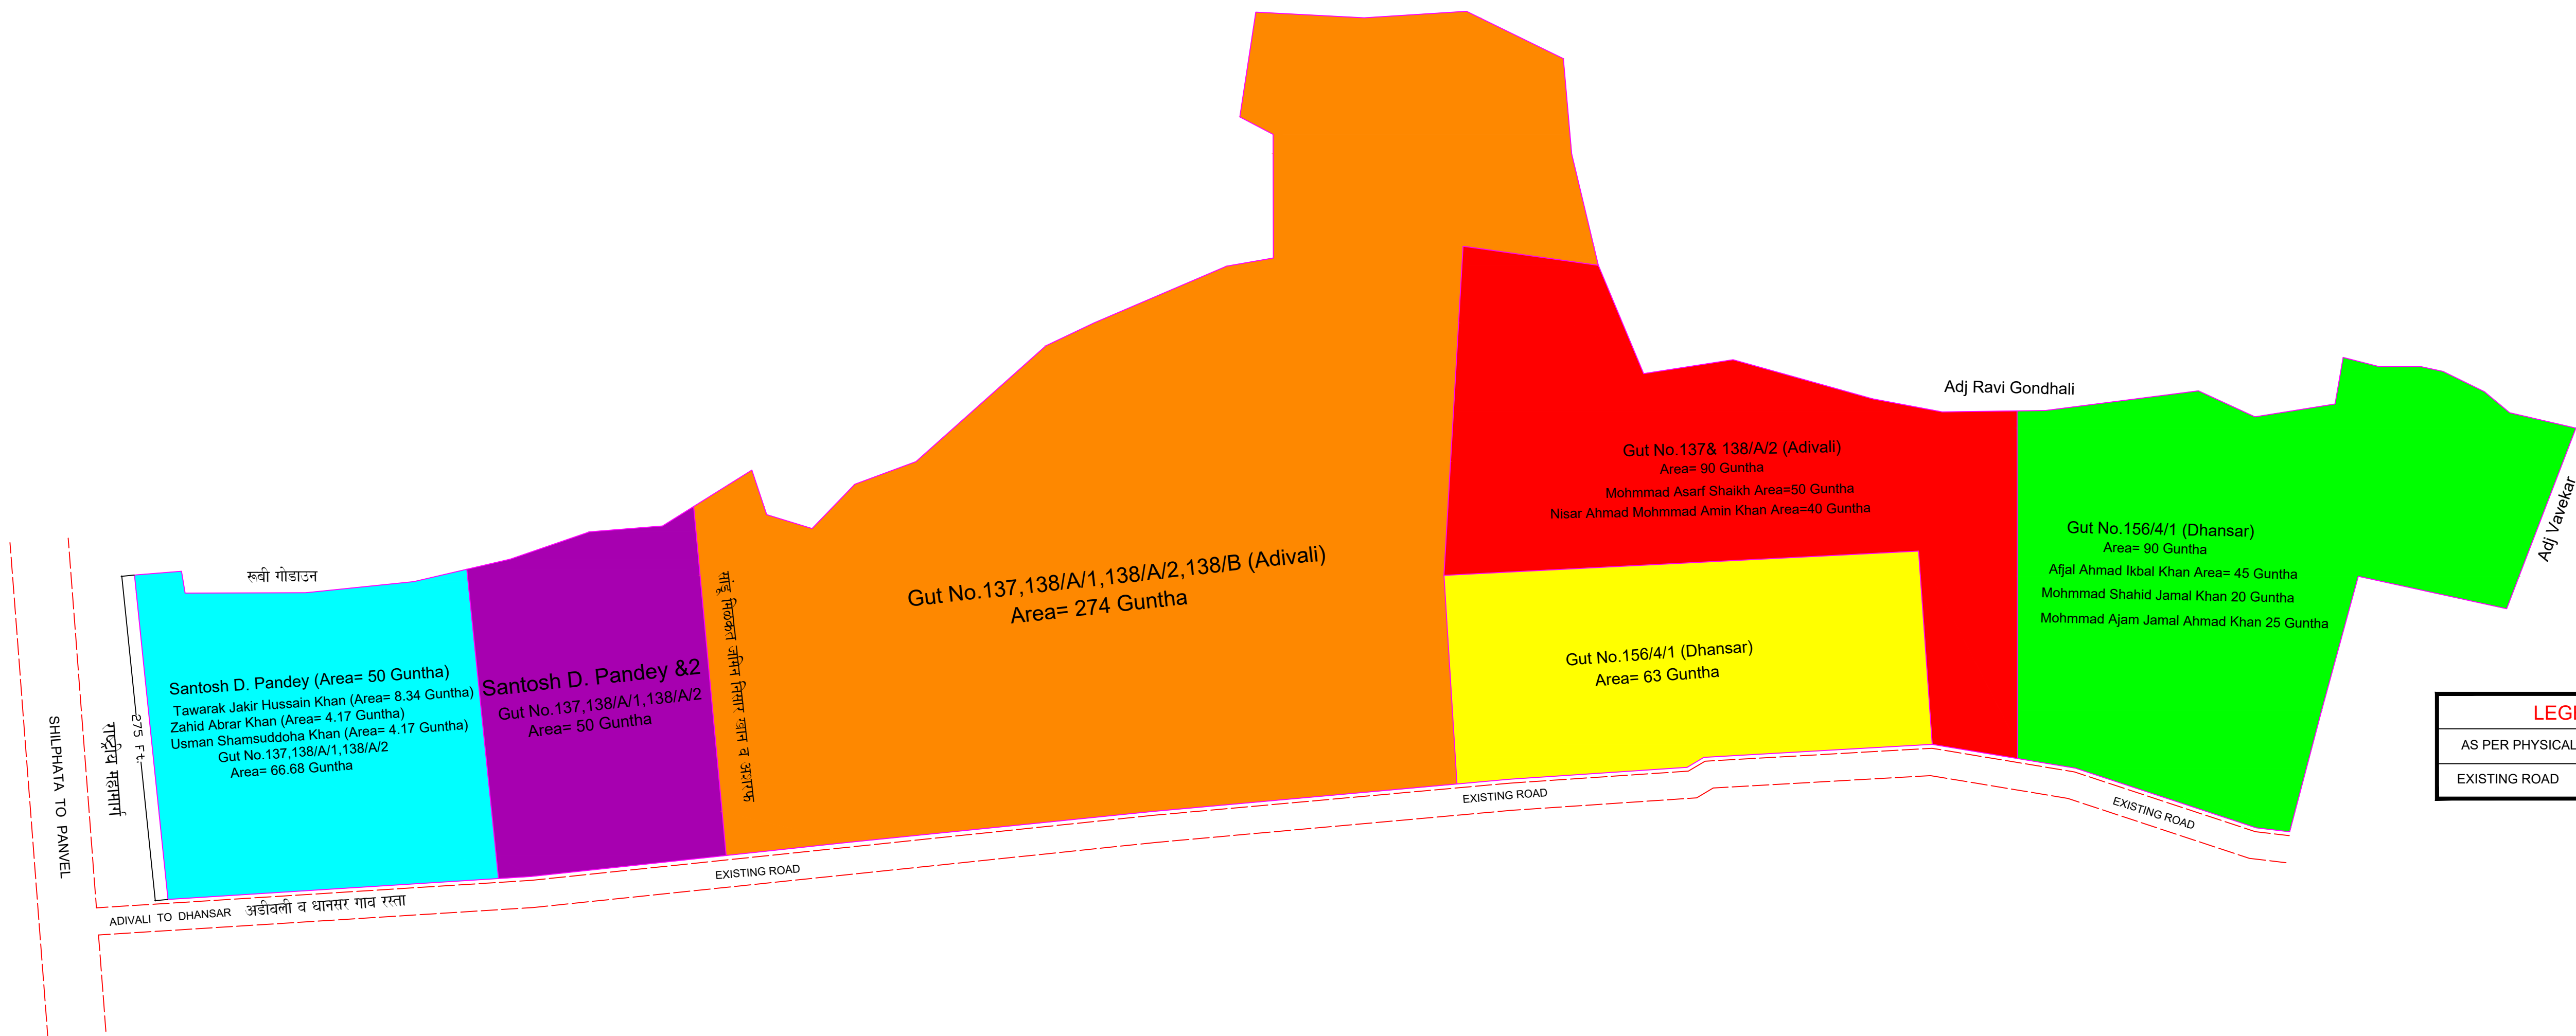

LEGEND	
AS PER PHYSICAL BOUNDRY	———
EXISTING ROAD	---

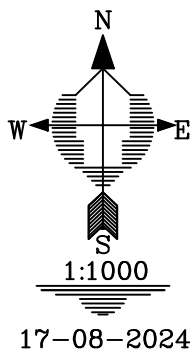

17-08-2024